
Ablution Block — Dimensioned FRONT ELEVATION (third angle, 1:50)

Three wall bays · octagonal vents set out · roof fascia band and raised central band · levels from ground level. Dimensions in millimetres.

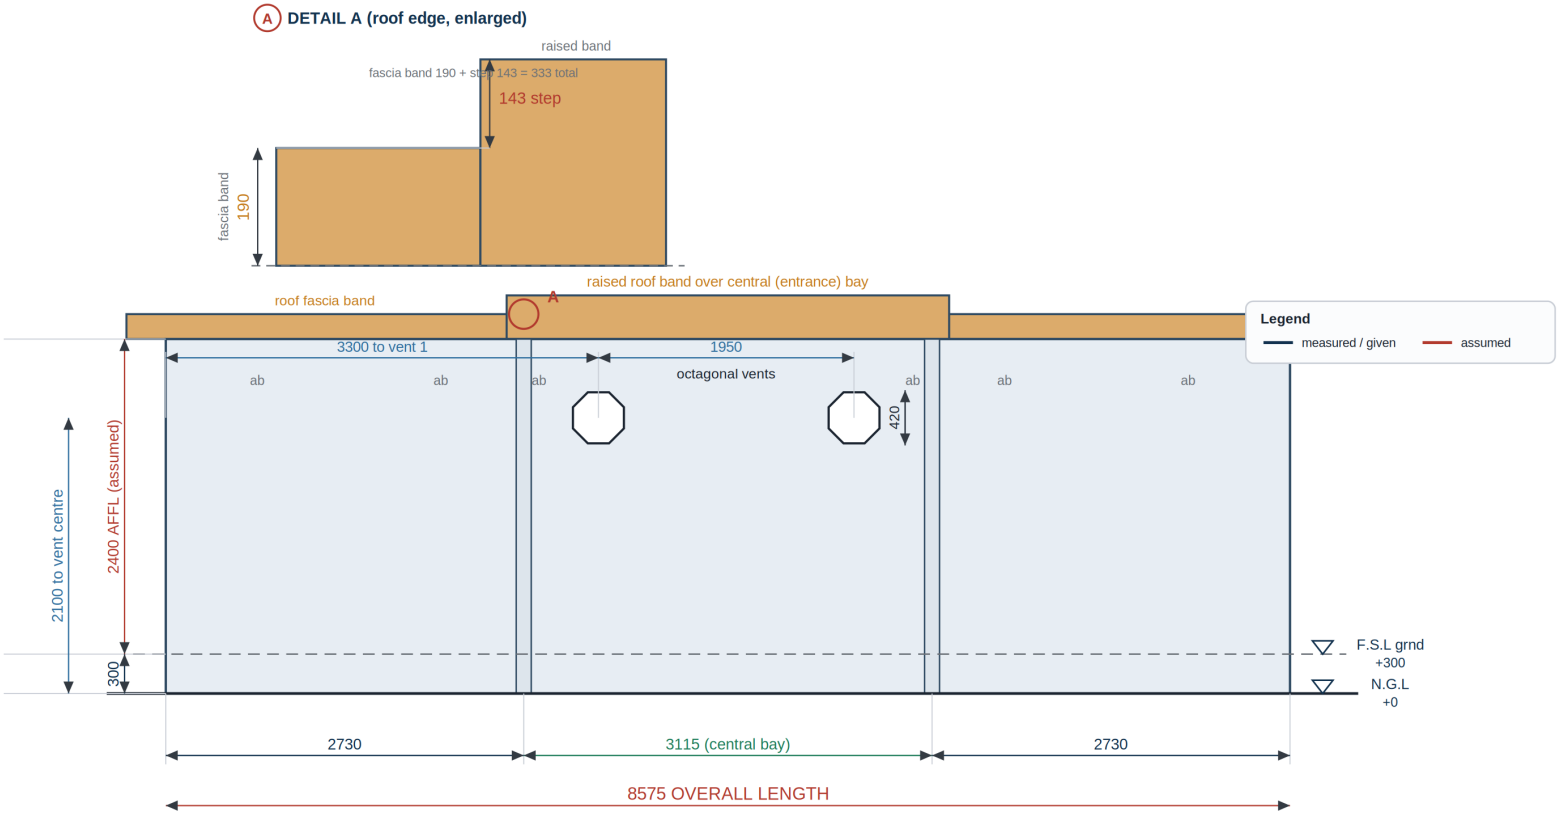

FRONT ELEVATION — fully dimensioned (mm)

Roof: 5° mono-pitch falls across the depth (shown true on the end elevation); on this face the eave reads horizontal. Central bay carries a raised roof band (+143).


Roof / elevation element	mm	Source	Element	mm	Source
Overall length	8575	given	**Roof fascia band depth**	190	measured
Side bays (each)	2730	measured	**Raised central band step**	143	measured
Central bay	3115	measured	**Octagon vents (across)**	420	measured
GL → finished floor	300	given	**Vent 1 / spacing**	3300 / 1950	measured
Wall height (FFL→eave)	2400	assumed	**Vent centre (AFFL)**	1800	assumed

Roof note: the roof is a 5° mono-pitch falling across the building depth (shown true on the end elevation). On this long face the eave reads horizontal; the central bay carries a raised roof/parapet band (+143). Mark “assumed” values on the sheet.

Ablution Block — Doors & Latrines (set-out)

Typical WC cubicle, door leaf sizes and fittings taken from the plan. Dimensions in millimetres.

TYPICAL WC CUBICLE (LATRINE) — plan

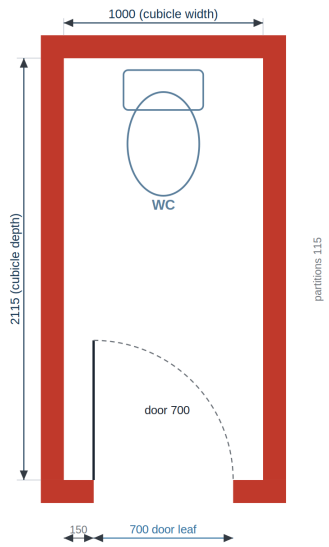

Door / element	Size (W×H)	No.	Notes
WC cubicle (latrine) door	700 × 2100	4	opens inward; 150 from partition; leaf measured ~700
Entrance door	900 × 2100	2	one per side, in the 1500 entrance opening + ramp
WC cubicle (latrine)	1000 × 2115	4	2 female + 2 male; WC pan at back wall
Urinals	~500 c/c	3	male side, back wall of central bay
Wash-hand basins (whb)	~450 wide	6	row of 3 each side, front wall
Partitions / walls	115	—	single-skin throughout
Entrance opening	1500 wide	2	given; ramp splay 40° (given)

Notes: cubicle 1000×2115 and entrance 1500 are figured on the plan; door leaf widths (700 cubicle, 900 entrance) and door heights (2100) are standard sizes scaled/assumed — letter these “ASSUMED” and adjust to any door schedule provided. All doors 2100 high unless specified. Cubicle doors open inward with the hinge 150 from the partition; the 40° ramp splay at each entrance is given on the plan.